



CLOSURE SLAB — PRECAST, 8" THICK, 45° ENDS

One per abutment. Stands in the back 8" of the bearing seat behind the girder ends and retains the approach fill.

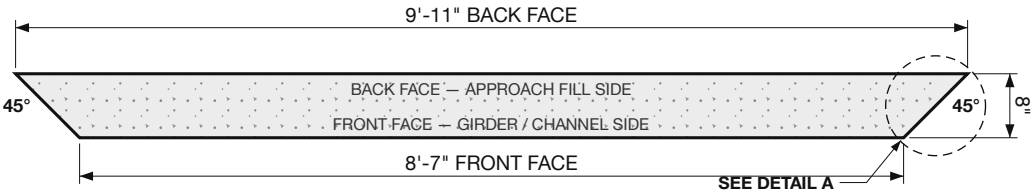

PLAN — AS INSTALLED


SCALE 1/2" = 1'-0"

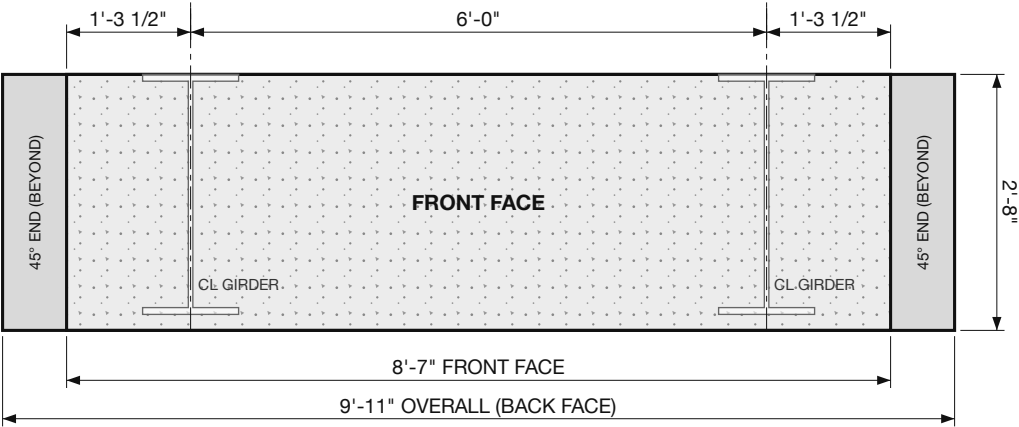

FRONT ELEVATION — FROM THE CHANNEL

SCALE 1/2" = 1'-0"

Girder ends shown for reference: tops flush with the slab top, soffits 2" above its bottom.

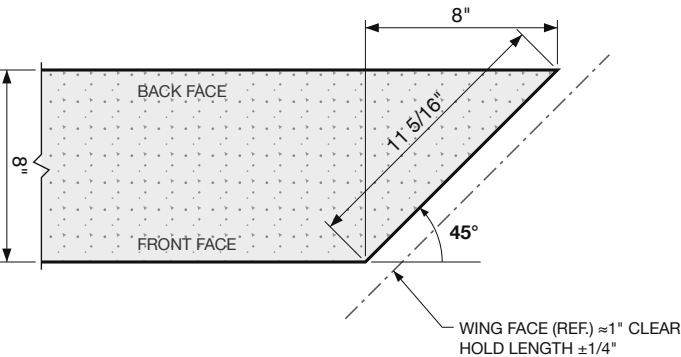


A DETAIL A — 45° END, IN PLAN

SCALE 1 1/2" = 1'-0"

PIECE DATA — EACH

Front face	8'-7"
Back face	9'-11"
Height	2'-8"
Thickness	8"
Ends	45° in plan
Volume	16.4 cu ft (0.61 CY)
Weight	≈ 2,470 lb @ 150 pcf
Quantity	2 — identical
Both pours	1.22 CY + waste

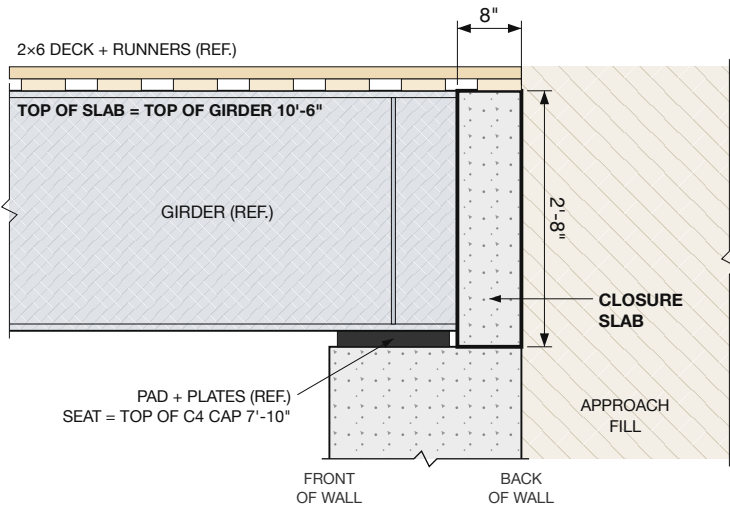

SECTION — AS INSTALLED (REFERENCE)

SCALE 1/2" = 1'-0"

NOTES

- Two pieces, identical — the slab is symmetric, so the same piece goes in at both abutments. One form, poured twice. Form layout is on Sheet 2.
- FRONT FACE (8'-7") faces the girder ends and the channel. BACK FACE (9'-11") faces the approach fill and finishes flush with the back of the wall.
- TOP EDGE carries the last 8" of deck and must finish flush with the girder tops — keep it straight and square. All edges square, no chamfers.
- 45° ENDS sit parallel to the splayed wings with only ≈1" clear each side. Hold length to ±1/4", height to ±1/8", thickness to +0 / -1/4".

HOLD — NOT IN THE BRIDGE MODEL, CONFIRM BEFORE POURING

- Reinforcing steel — size, spacing, cover.
- Girder-end ties — embeds or sleeves at the girder lines (3'-0" each side of the slab CL). May need block-outs in the form.
- Lifting / tip-up inserts — piece is ≈2,470 lb.
- Concrete mix and strength.

PROJECT

ATV BRIDGE — 90' SPAN

SHEET

CLOSURE SLAB — PIECE DRAWING

QTY

2 — identical

DATE

2026-10-07

REV

0

SHEET

1 of 2


Dimensions govern — do not scale. Scales are true only when printed at 100% on 11x8.5.

Drawn by:

Checked:


FORM — CAST FLAT, FRONT FACE DOWN

The bed forms the front face. The ends flare out 45° as the pour comes up, so the screeded top is the 9'-11" back face.

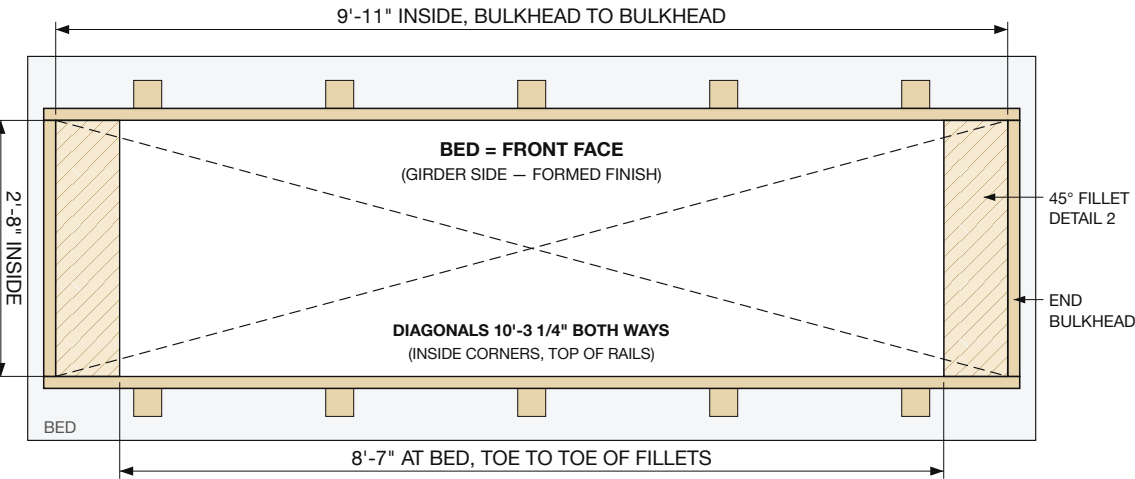


1 FORM PLAN — LOOKING DOWN INTO THE FORM

SCALE 1/2" = 1'-0"

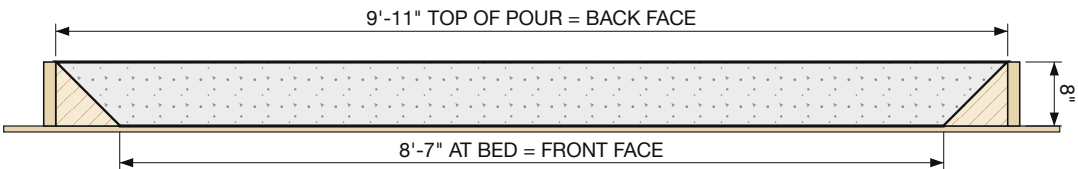


2A FORM SECTION — LENGTHWISE

SCALE 1/2" = 1'-0"

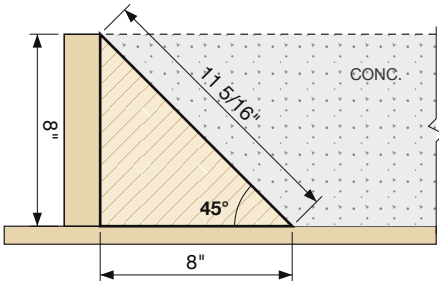

2 DETAIL 2 — 45° END FILLET

SCALE 1 1/2" = 1'-0"

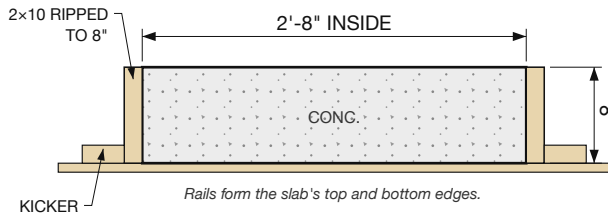

2B SECTION ACROSS FORM

SCALE 3/4" = 1'-0"

FORM MATERIALS (SUGGESTED)

- Bed** Flat, level shop floor, or 3/4" MDO/ply on sleepers, min 4'-0" x 11'-0". Tape and fill any sheet seams — the bed is the visible front face.
- Side rails (2)** 2x10 ripped to exactly 8", 10'-2" long (run past the bulkheads).
- Bulkheads (2)** 2x10 ripped to exactly 8", 2'-8" long, fit between rails.
- Fillets (2)** 45° triangle, 8" x 8" legs, 2'-8" long. Solid wood, or a 3/4" ply face on gussets with 6 15/16" legs (ply ripped 11 5/16" on its face, both edges beveled 45°).
- Kickers** 2x4 blocks screwed to the bed against the rails, 2'-0" o.c. max.

BUILD AND CHECK

- Set the bed flat and level — 1/8" max over the length.
- Snap the inside rectangle 9'-11" x 2'-8". Set rails and bulkheads to it, tops exactly 8" above the bed all the way around.
- Square it: inside diagonals at the top of the rails 10'-3 1/4" both ways.
- Fix the fillets tight to the bulkheads — formed face runs from 8" in at the bed to the top inside corner of the bulkhead. Check 8'-7" toe to toe at the bed.
- Caulk the seams, oil every contact face with form release.
- STOP — set steel, tie embeds and lift inserts per the HOLD items on Sheet 1.**
- Pour, vibrate, screed off the rails. Float finish the top (back face — goes against fill).
- After stripping: front face 8'-7", back face 9'-11", height 2'-8", thickness 8". Mark FRONT on the bed face before tipping up.

POUR

0.61 CY per slab, 1.22 CY for both — allow ~10% for waste. ≈2,470 lb each.

HOLD — CONFIRM BEFORE POURING (SHEET 1)

Rebar · girder-end tie embeds (may need block-outs in the rails or bed) · lift/tip-up inserts · concrete mix. Build the form now; leave it open until these are set.

PROJECT
ATV BRIDGE — 90' SPAN

SHEET
CLOSURE SLAB — FORM LAYOUT

QTY
2 — identical

DATE
2026-10-07

REV
0

SHEET
2 of 2

Dimensions govern — do not scale. Scales are true only when printed at 100% on 11x8.5.

Drawn by:

Checked: